


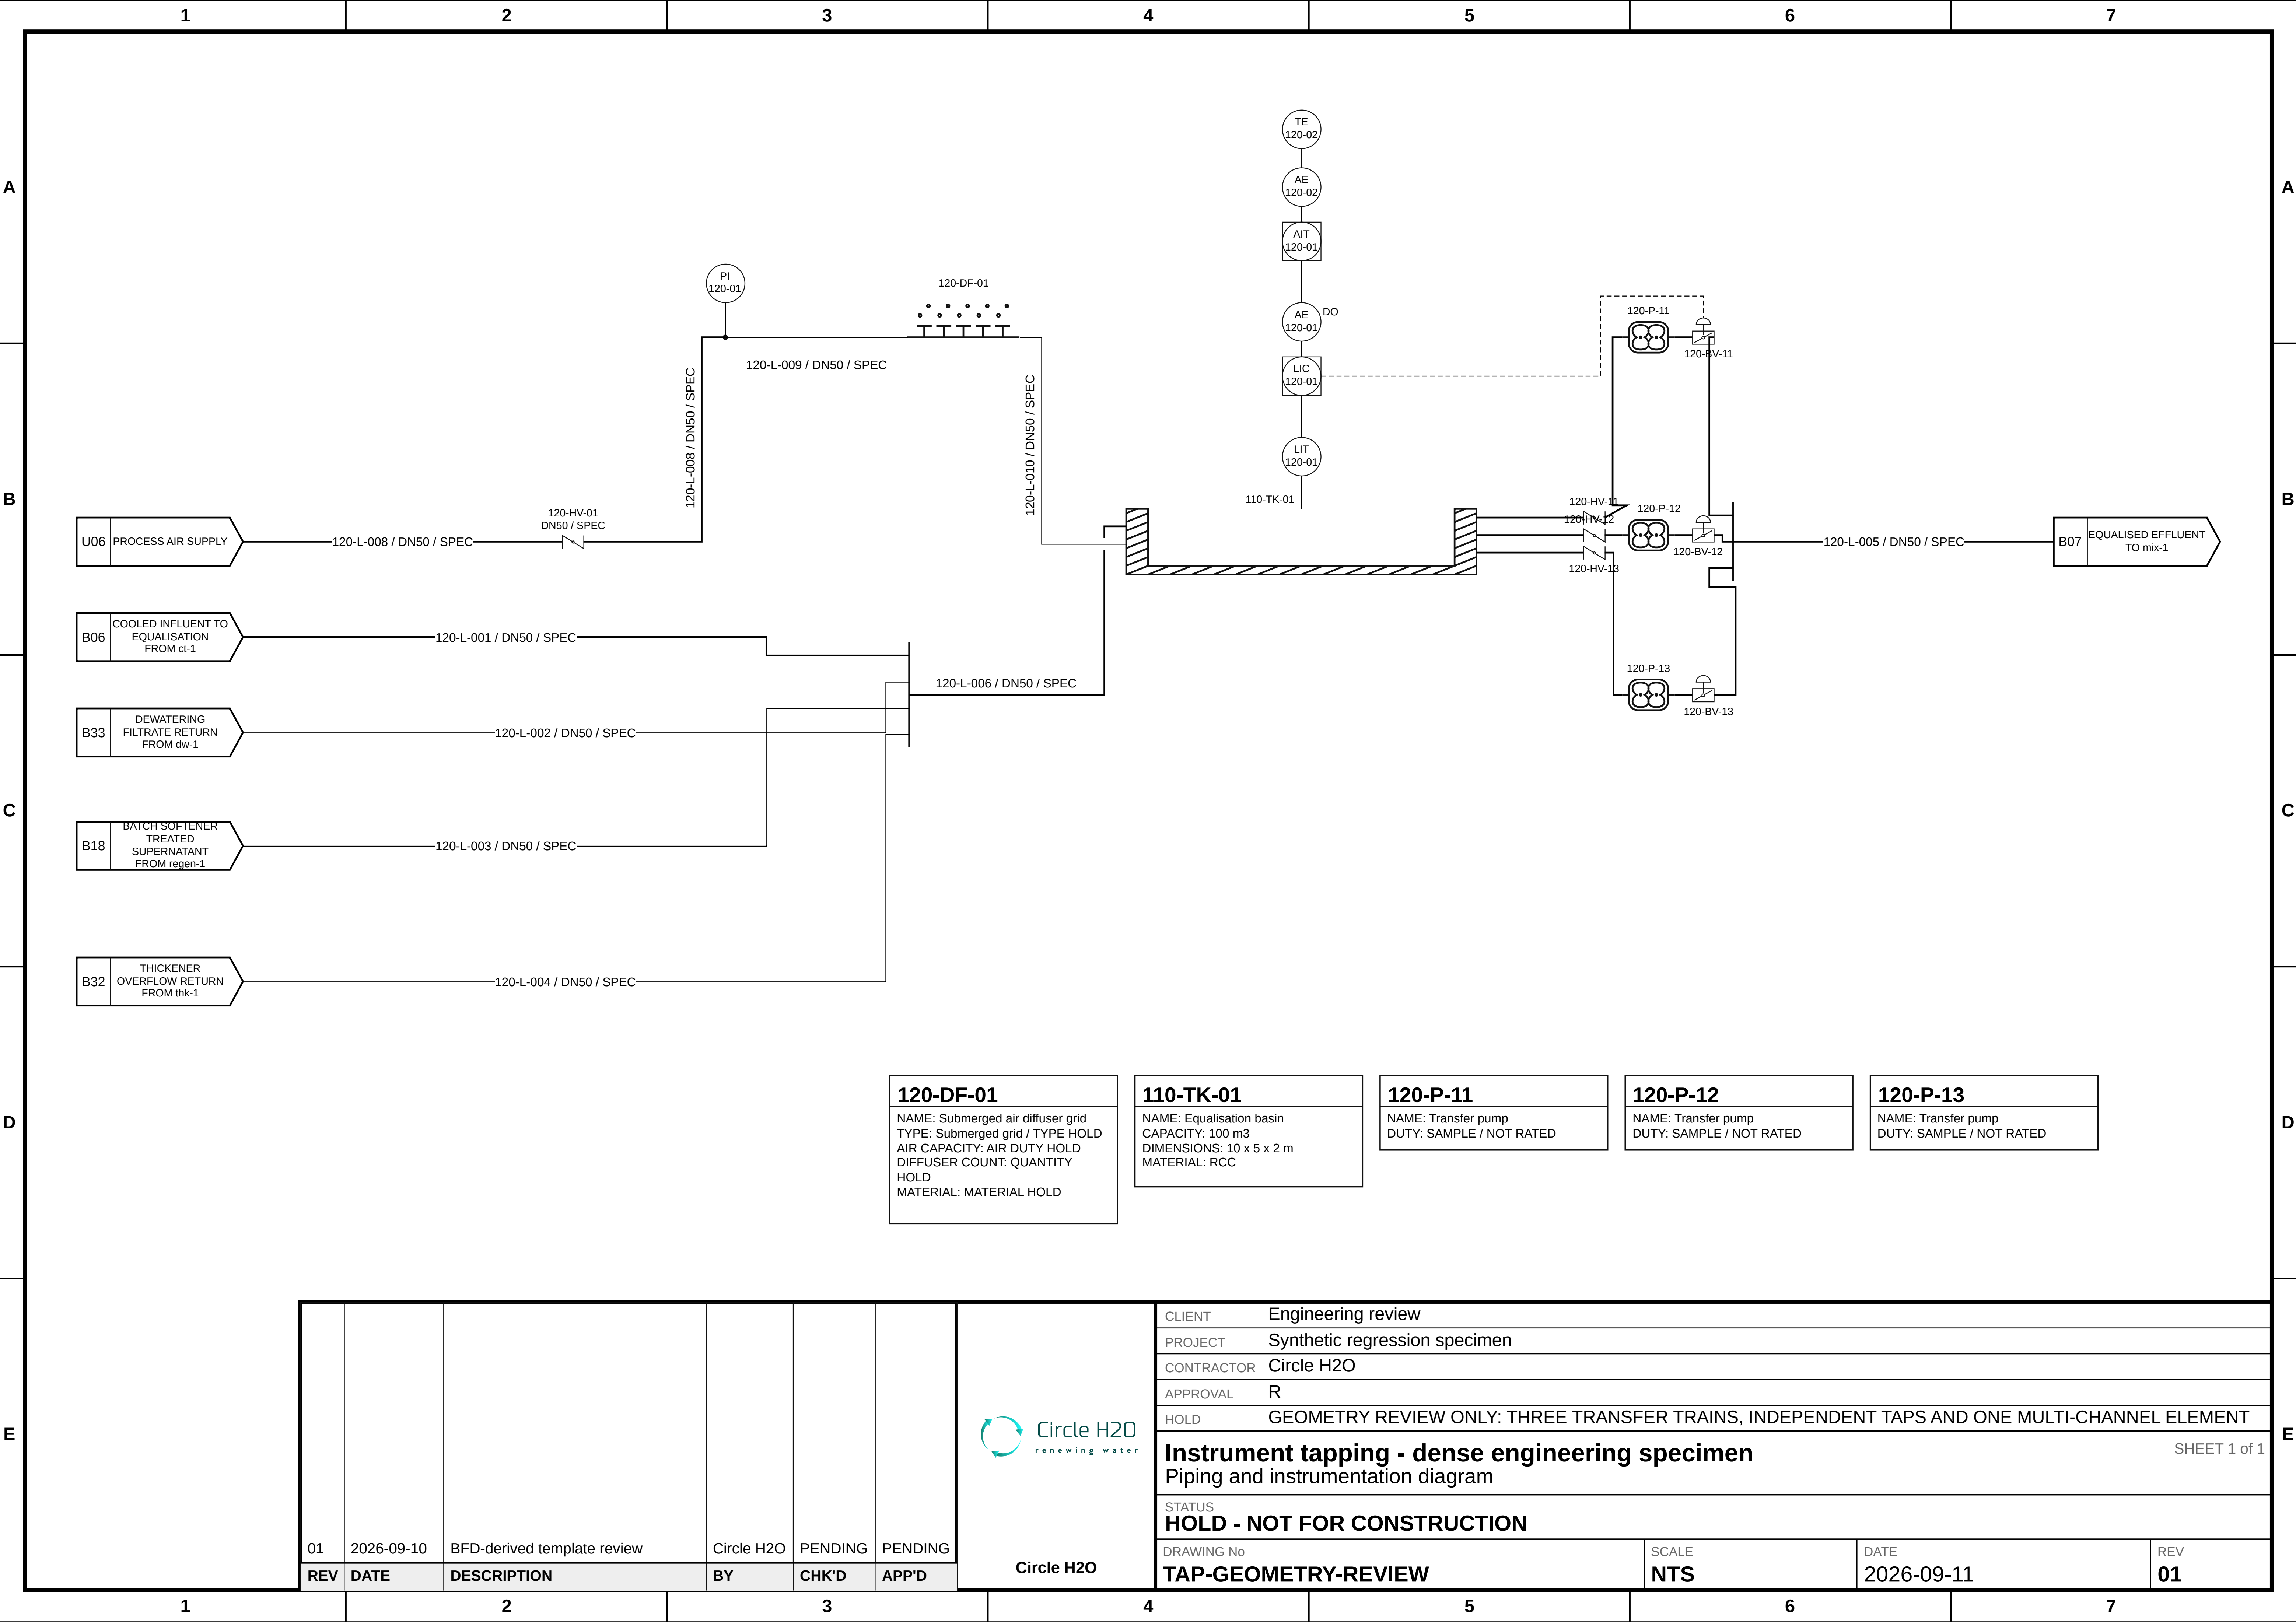

120-DF-01

NAME: Submerged air diffuser grid
TYPE: Submerged grid / TYPE HOLD
AIR CAPACITY: AIR DUTY HOLD
DIFFUSER COUNT: QUANTITY HOLD
MATERIAL: MATERIAL HOLD

110-TK-01

NAME: Equalisation basin
CAPACITY: 100 m3
DIMENSIONS: 10 x 5 x 2 m
MATERIAL: RCC

120-P-11

NAME: Transfer pump
DUTY: SAMPLE / NOT RATED

120-P-12

NAME: Transfer pump
DUTY: SAMPLE / NOT RATED

120-P-13

NAME: Transfer pump
DUTY: SAMPLE / NOT RATED

01	2026-09-10	BFD-derived template review	Circle H2O	PENDING	PENDING	Circle H2O renewing water Circle H2O	CLIENTEngineering review							
							PROJECTSynthetic regression specimen							
							CONTRACTORCircle H2O							
							APPROVALR							
							HOLDGEOMETRY REVIEW ONLY: THREE TRANSFER TRAINS, INDEPENDENT TAPS AND ONE MULTI-CHANNEL ELEMENT							
							Instrument tapping - dense engineering specimen Piping and instrumentation diagram SHEET 1 of 1							
REV	DATE	DESCRIPTION	BY	CHK'D	APP'D	Circle H2O	STATUS		HOLD - NOT FOR CONSTRUCTION					
							DRAWING NoTAP-GEOMETRY-REVIEW			SCALENTS	DATE2026-09-11		REV01	